


LEGEND

B LED BULKHEAD LIGHT FITTING C/W BATTERY PACK (SURFACE MOUNTED)

Note:

The battery pack emergency LED light fittings are to be circuit to DB-CP3/L1 & DB-CP3/L2. Tenderers shall deem this requirement included in their scope of works, including all necessary cabling, terminations, and associated accessories for a complete and functional installation.

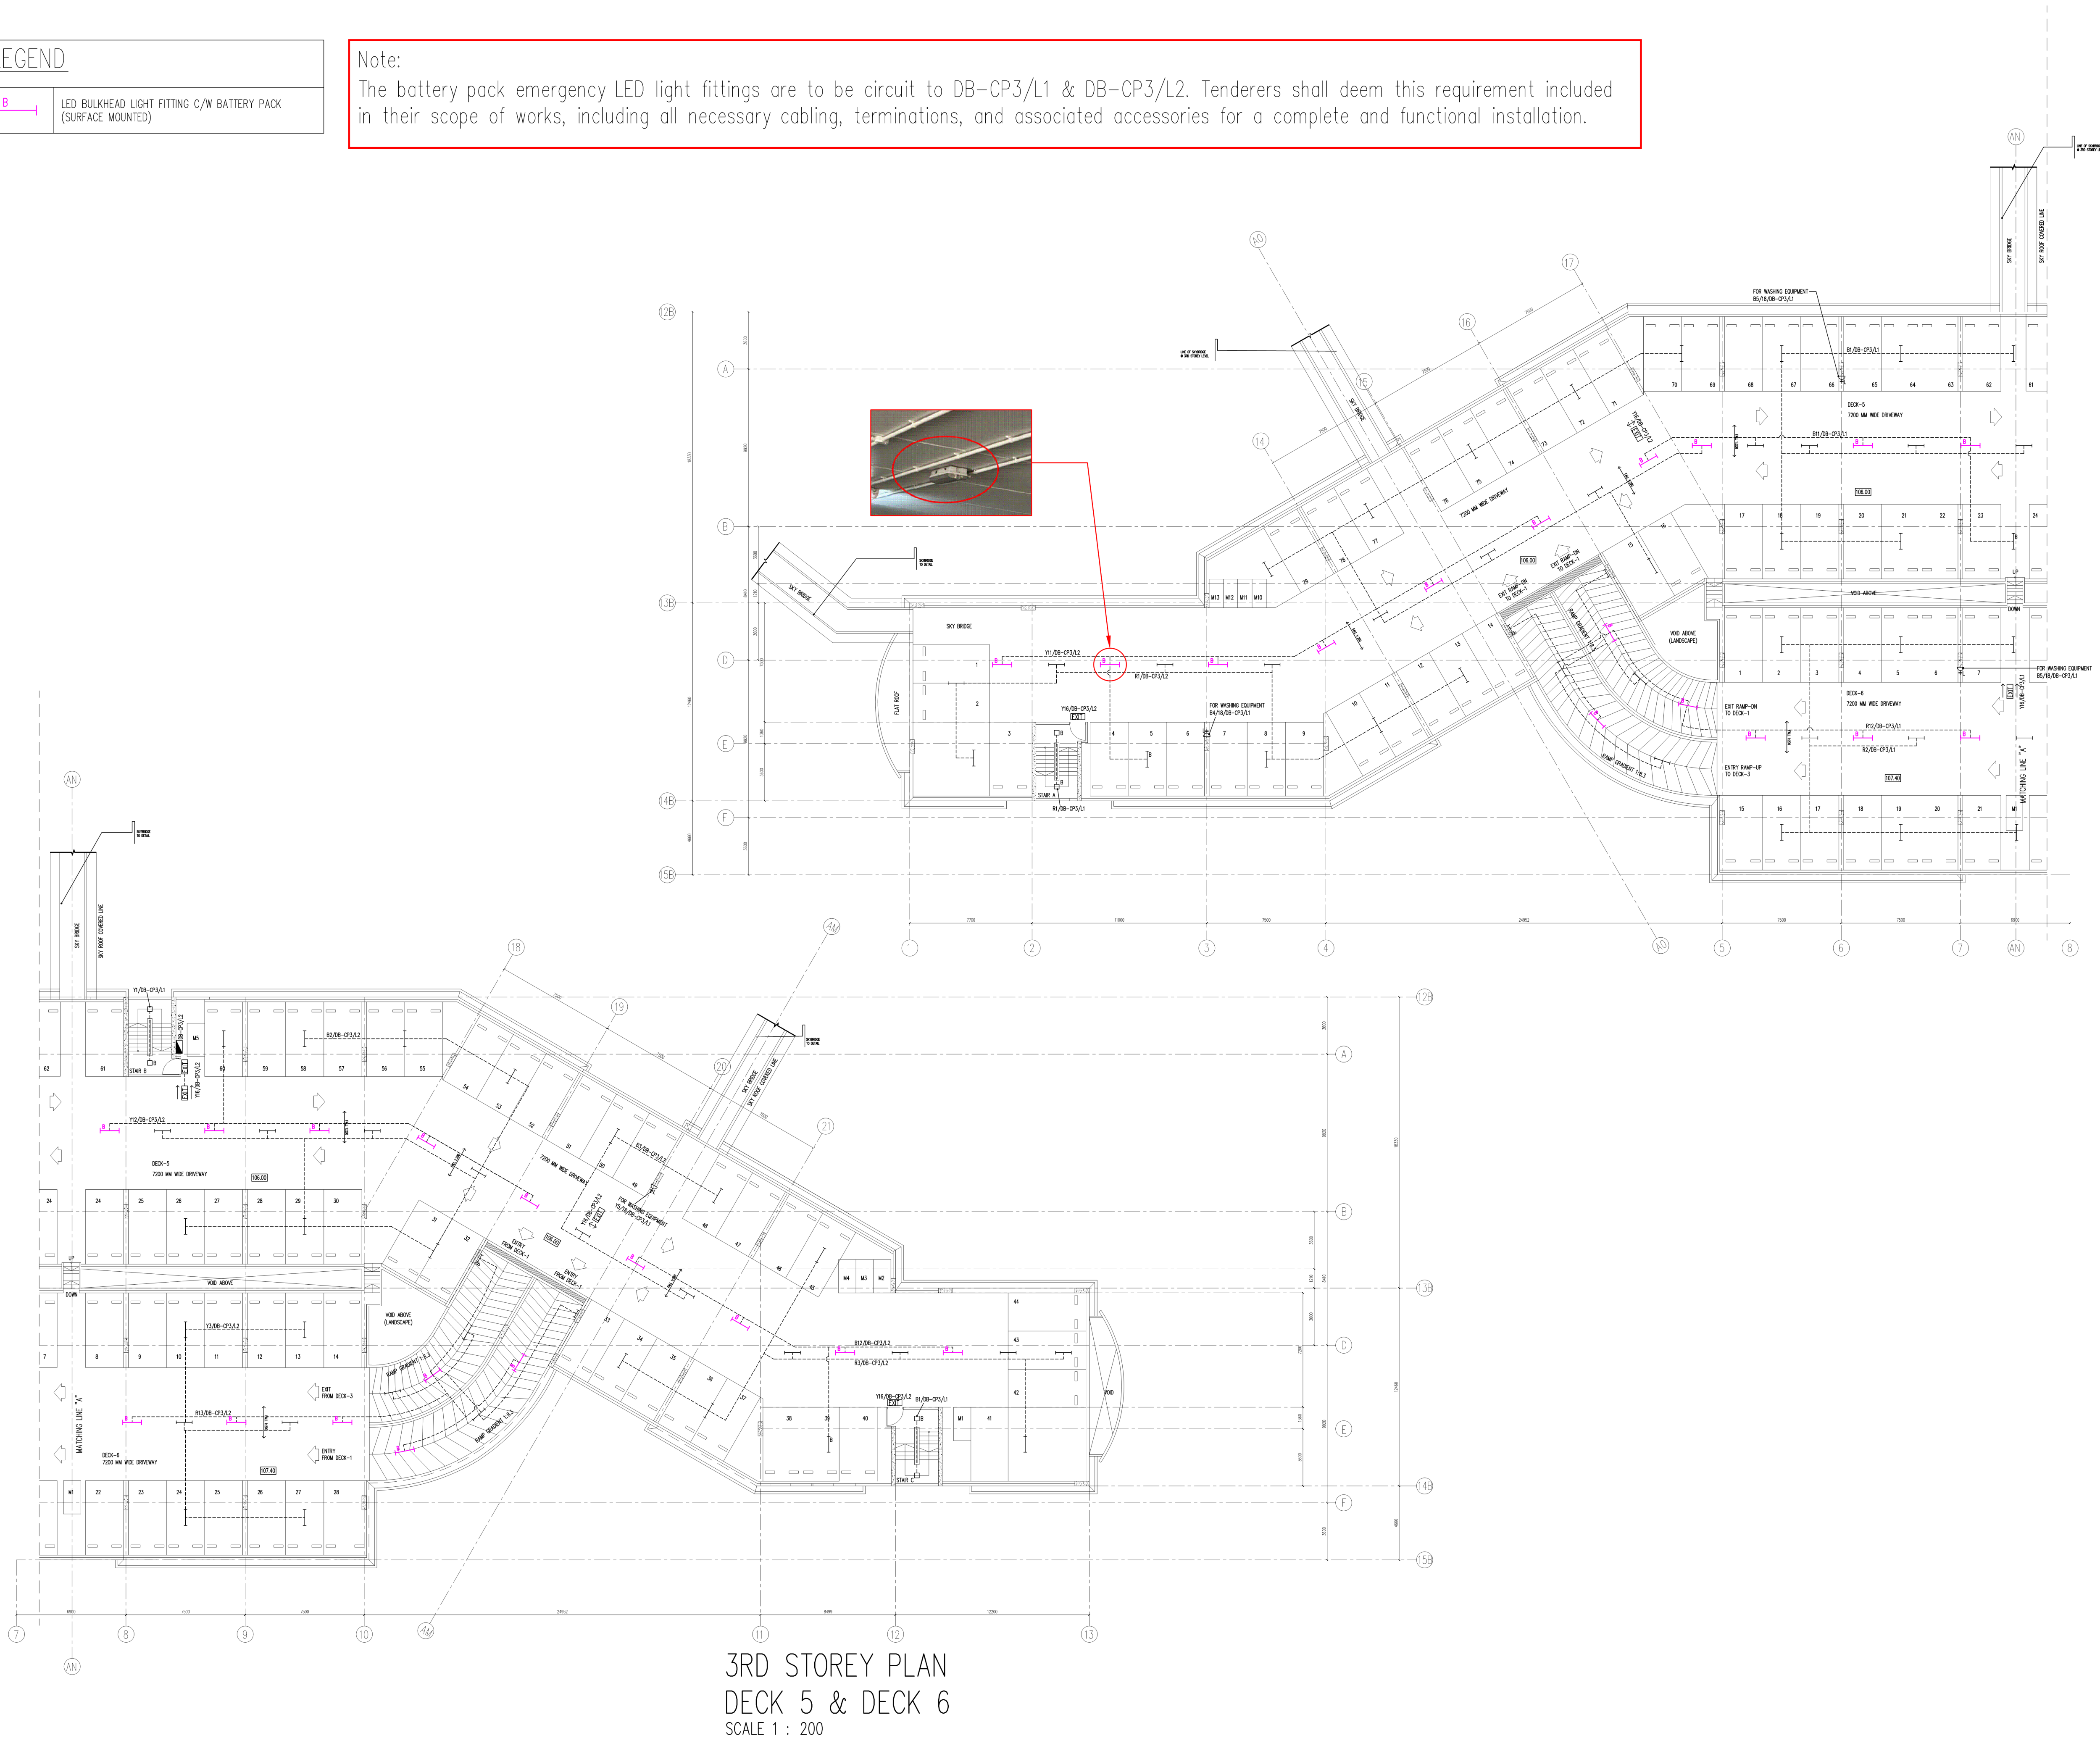

3RD STOREY PLAN
DECK 5 & DECK 6
SCALE 1 : 200

TENDER DRAWING
NOVEMBER 2025

REV DATE DRAWN CHECKED DESCRIPTION

TENDER DRAWING

CLIENT:



HDB HUB 480 LORONG 6 TOA PAYOH SINGAPORE 310480

CLIENT SIGNATURE:

DRAWING NO. HB-N2303-B78-E-203 REVISION: -

PROJECT TITLE:

MECHANICAL AND ELECTRICAL
CYCLICAL IMPROVEMENT WORKS
TO MULTI-STOREY CAR PARKS
(BATCH 34)

DRAWING TITLE: (FOR EST BLK NO 769AMSCP)

ELECTRICAL INSTALLATION

LIGHTING AND POWER LAYOUT

3RD STOREY PLAN DECK 5 & DECK 6

SCALE: AS SHOWN DATE: NOVEMBER 2025

DRAWN BY: TLY CHECKED BY: JL/NC

M & E CONSULTANT:



CCA & Partners Pte Ltd
M&E Consulting Engineer
46 Lorong 17 Geylang, #02-02, Enterprise Industrial Building,
Singapore 388566, Tel: 6476 2272 Fax: 6475 6229
E-mail : cca@cheetoon.com

C&S ENGINEER:



(Professional Engineers, Project Management and
and Structural Inspection)
Blk 28, Sin Ming Lane,
#07-137, Midview City,
Singapore 573972
Tel: (65) 6459 5438 Fax: (65) 6459 5267
Email: info@aoconsultants.com

QUANTITY SURVEYOR:

QS Consultants Pte Ltd

21 Bukit Batok Crescent
#16-70, WCEGA Tower
Singapore 658065
Tel: 6899 4298 Fax: 6899 4981
E-mail : qs@qsconsultants.sg


DRAWING NO. HB-N2303-B78-E-203 REVISION: -

DESIGN ENGINEER QUALIFIED PERSON

© copyright cca & partners pte ltd

LEGEND	
	LED BULKHEAD LIGHT FITTING C/W BATTERY PACK (SURFACE MOUNTED)

Note:
The battery pack emergency LED light fittings are to be circuit to DB-CP3/L1 & DB-CP3/L2. Tenderers shall deem this requirement included in their scope of works, including all necessary cabling, terminations, and associated accessories for a complete and functional installation.

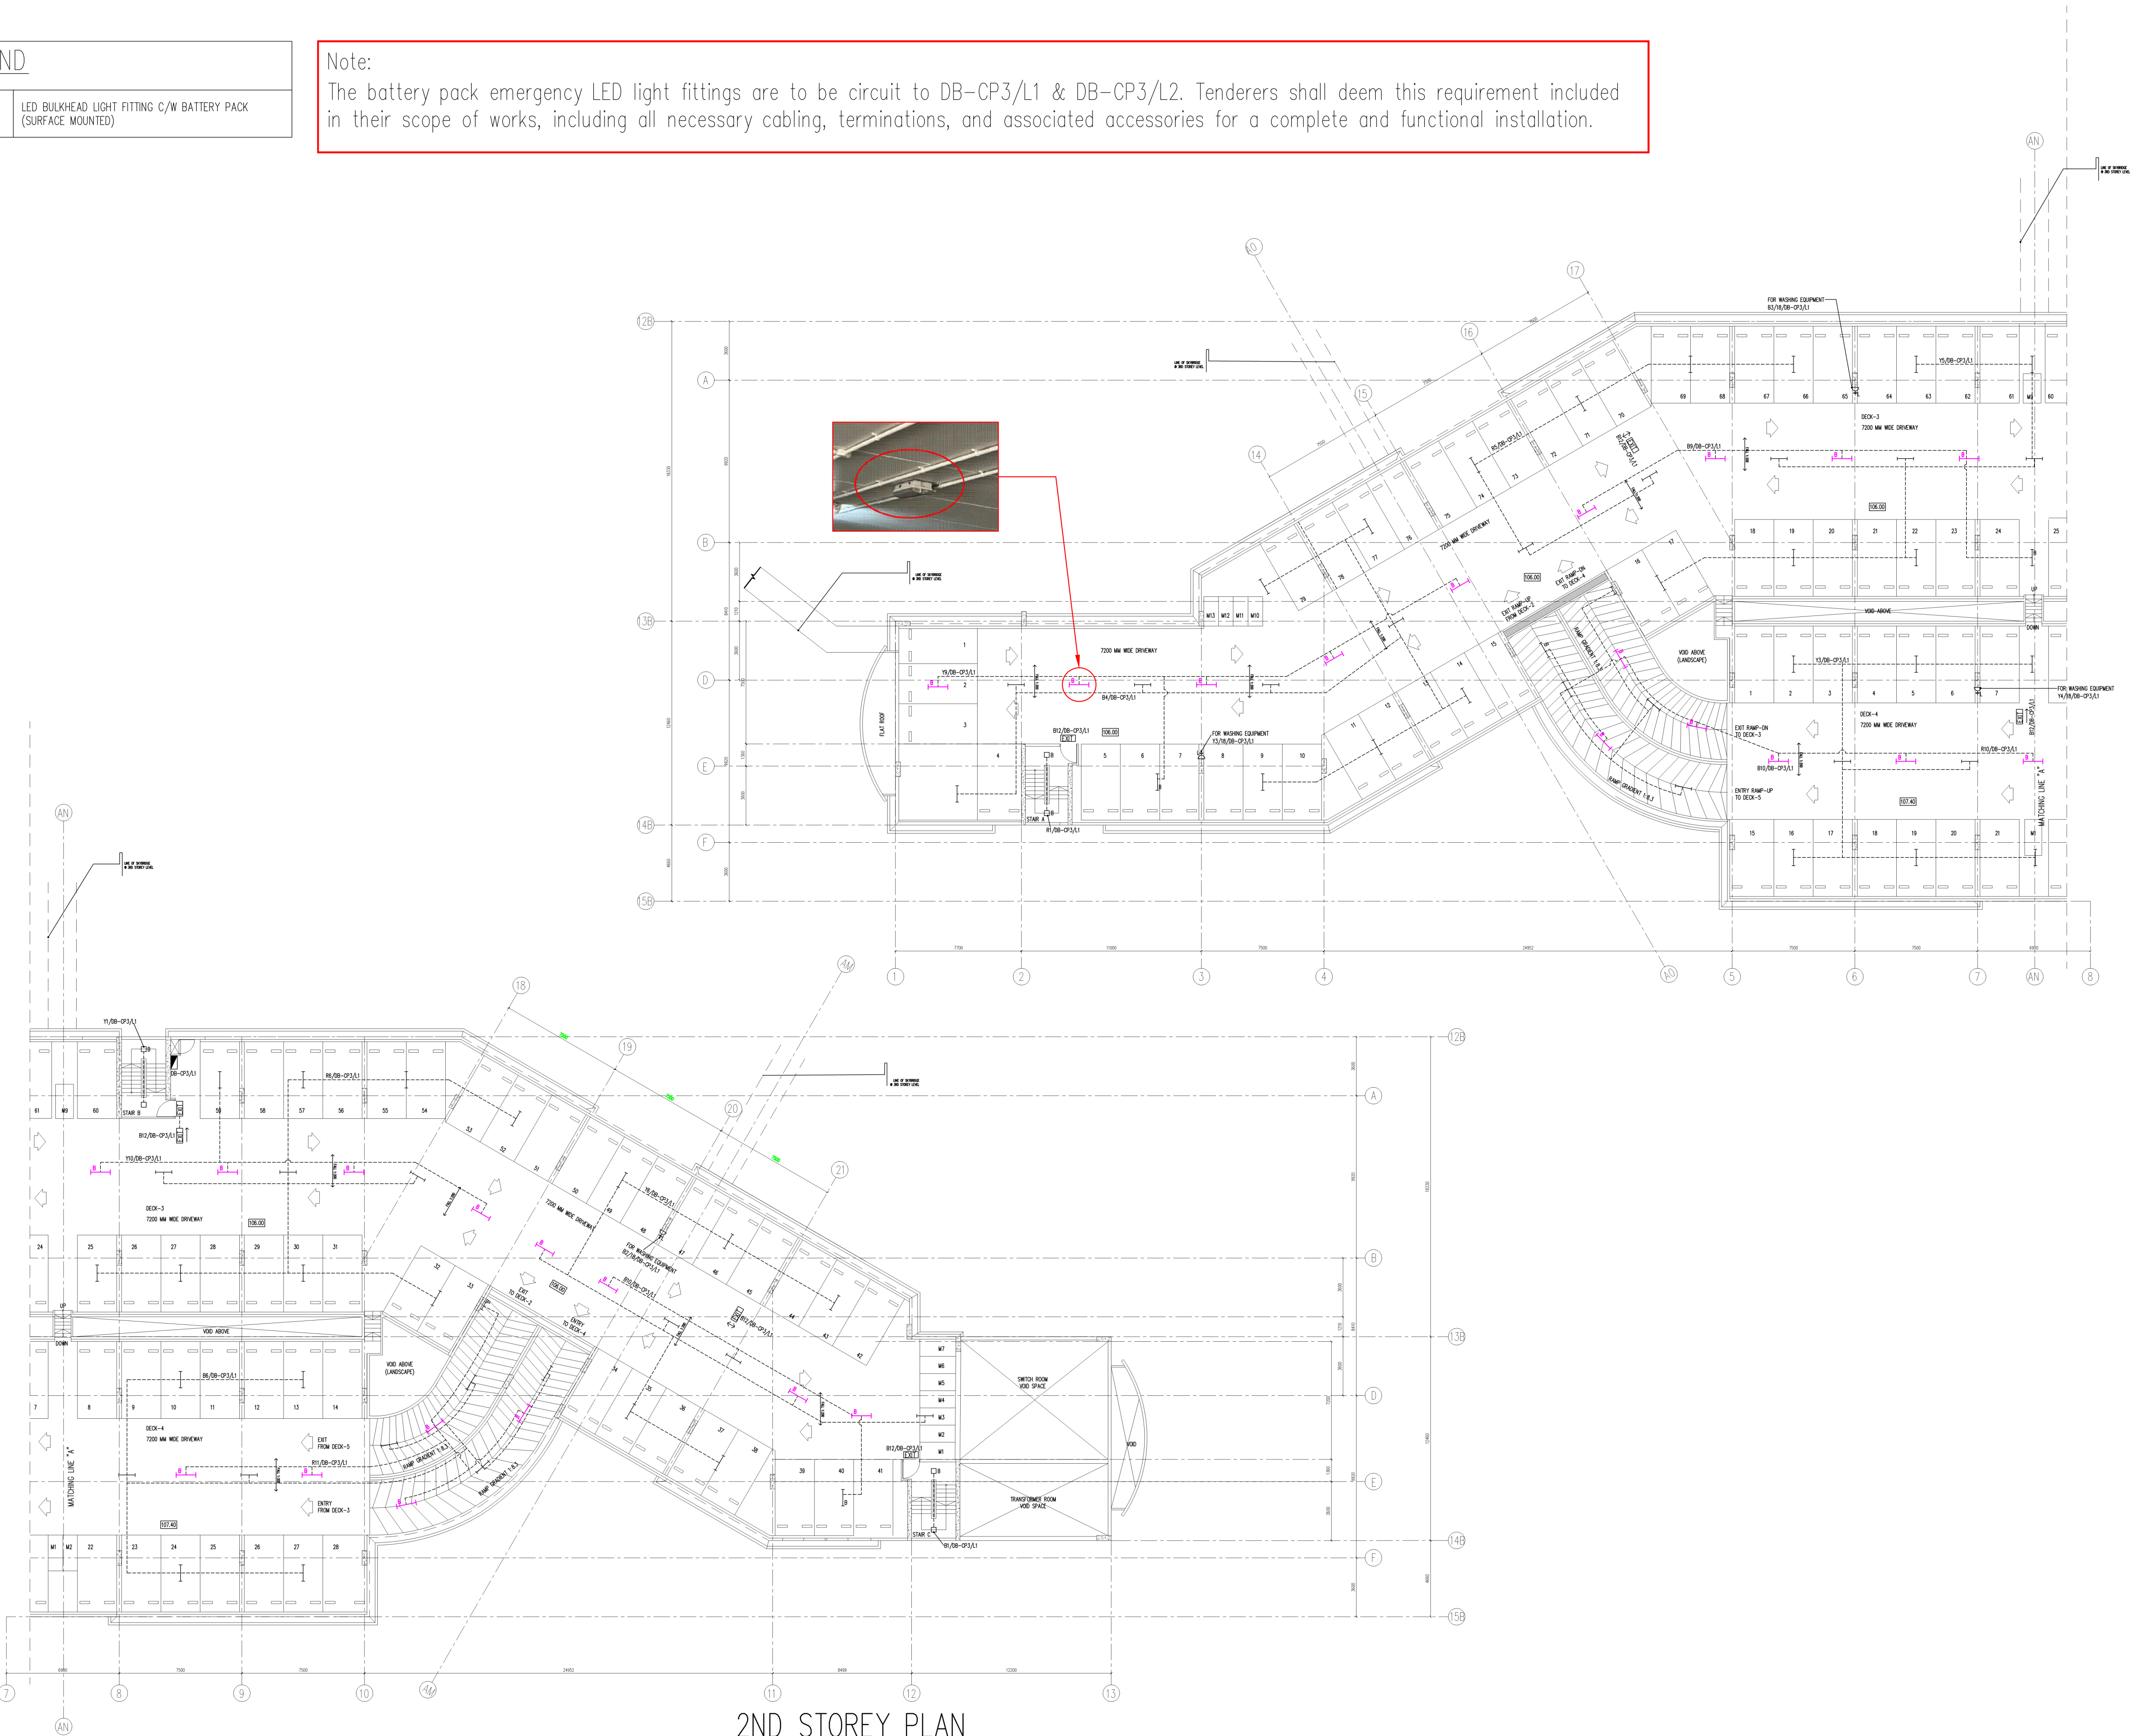

2ND STOREY PLAN
DECK 3 & DECK 4
SCALE 1 : 200

TENDER DRAWING
NOVEMBER 2025

REV	DATE	DRAWN	CHECKED	DESCRIPTION
TENDER DRAWING				

CLIENT:

**HOUSING & DEVELOPMENT BOARD**

HDB HUB 480 LORONG 6 TOA PAYOH SINGAPORE 310480
CLIENT SIGNATURE:

DRAWING NO. HB-N2303-B78-E-202	REVISION: -
--------------------------------	-------------

PROJECT TITLE:
MECHANICAL AND ELECTRICAL CYCLICAL IMPROVEMENT WORKS TO MULTI-STOREY CAR PARKS (BATCH 34)

DRAWING TITLE: (FOR EST BLK NO 769AMSCP)
ELECTRICAL INSTALLATION LIGHTING AND POWER LAYOUT 2ND STOREY PLAN DECK 3 & DECK 4

SCALE: AS SHOWN	DATE: NOVEMBER 2025
DRAWN BY: TLY	CHECKED BY: JL/NC

M & E CONSULTANT:
CCAPpartners

CCA & Partners Pte Ltd
M&E Consulting Engineer
46 Lorong 17 Geylang, #02-02, Enterprise Industrial Building,
Singapore 388568, Tel: 6476 2272 Fax: 6475 6229
E-mail : cca@cheetoon.com

C&S ENGINEER:
ANG & ONG
CONSULTANTS PTE LTD
(Professional Engineers, Project Management and
and Structural Inspection)

Blk 28, Sin Ming Lane,
#07-137, Midview City,
Singapore 573972
Tel: (65) 6459 5438 Fax: (65) 6459 5267
Email: info@aoconsultants.com

QUANTITY SURVEYOR:
QS Consultants Pte Ltd

21 Bukit Batok Crescent
#16-70, WCEGA Tower
Singapore 658065
Tel: 6899 4298 Fax: 6899 4981
E-mail : qs@qsconsultants.sg

DRAWING NO. HB-N2303-B78-E-202	REVISION: -
--------------------------------	-------------


DESIGN ENGINEER QUALIFIED PERSON

LEGEND

B LED BULKHEAD LIGHT FITTING C/W BATTERY PACK (SURFACE MOUNTED)

Note:

The battery pack emergency LED light fittings are to be circuit to DB-CP3/L1 & DB-CP3/L2. Tenderers shall deem this requirement included in their scope of works, including all necessary cabling, terminations, and associated accessories for a complete and functional installation.

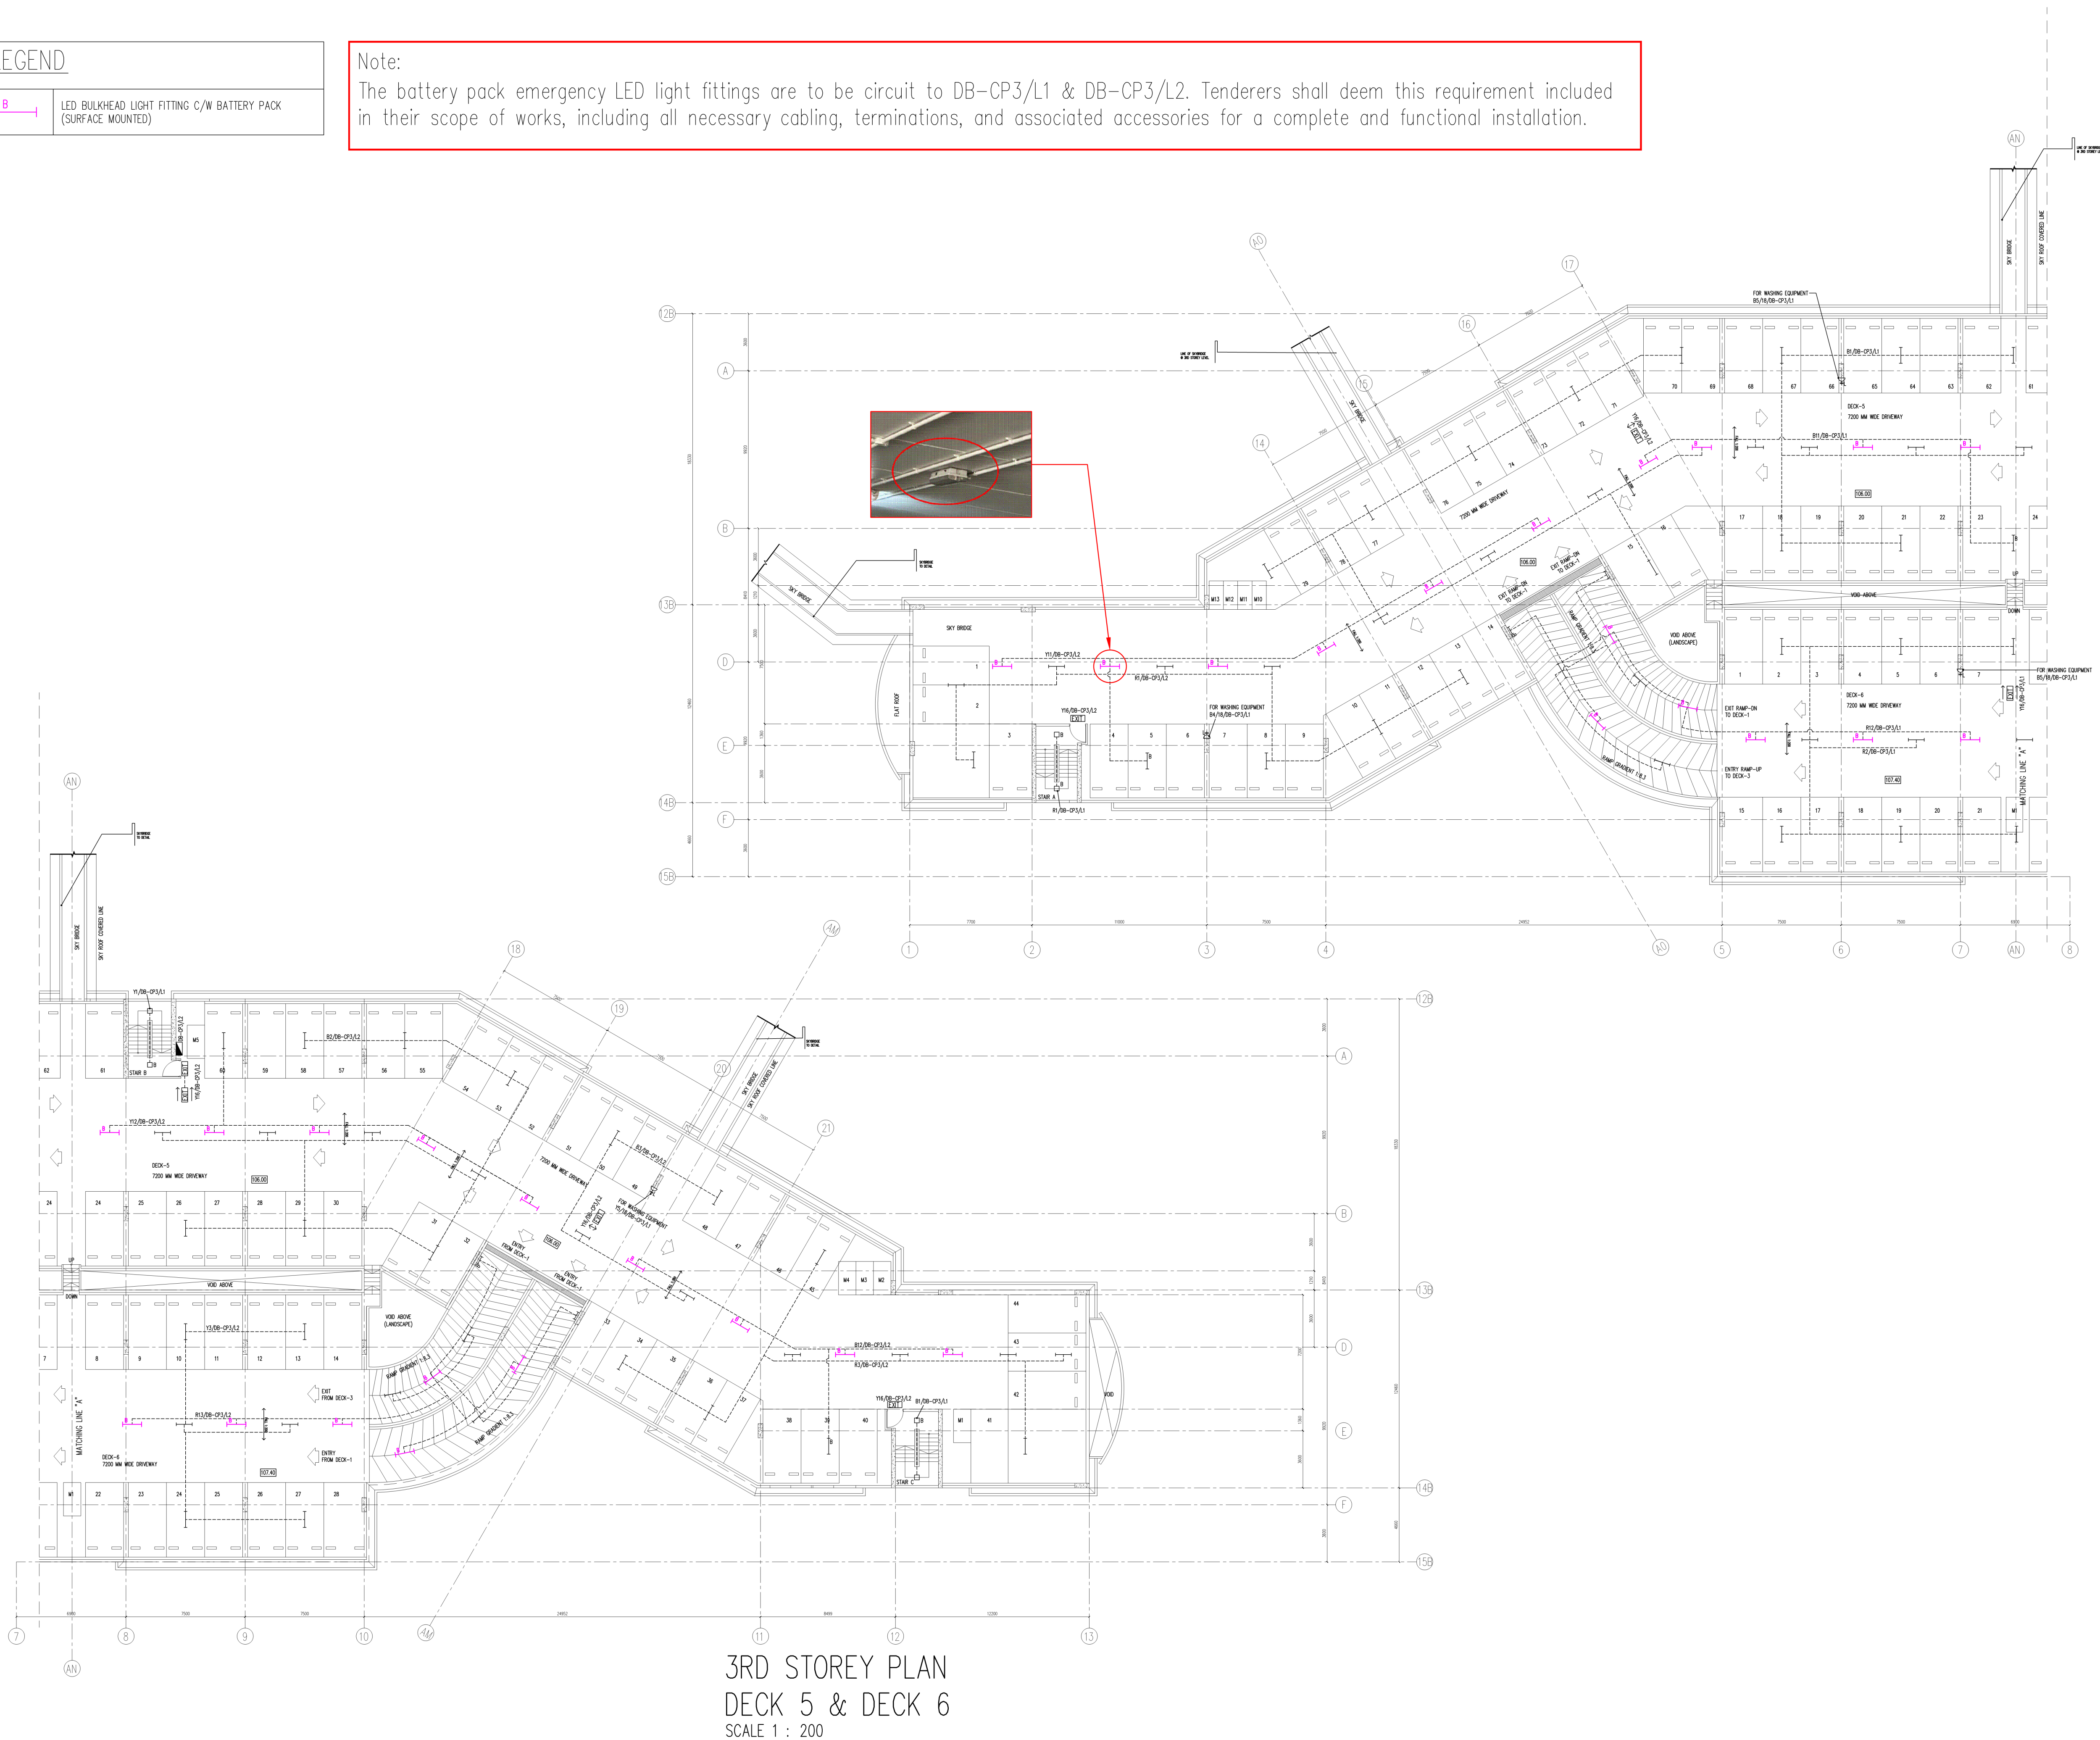

TENDER DRAWING
NOVEMBER 2025

REV DATE DRAWN CHECKED DESCRIPTION

TENDER DRAWING

CLIENT:



HDB HUB 480 LORONG 6 TOA PAYOH SINGAPORE 310480

CLIENT SIGNATURE:

DRAWING NO. HB-N2303-B78-E-203 REVISION: -

PROJECT TITLE:

MECHANICAL AND ELECTRICAL
CYCLICAL IMPROVEMENT WORKS
TO MULTI-STOREY CAR PARKS
(BATCH 34)

DRAWING TITLE: (FOR EST BLK NO 769AMSCP)

ELECTRICAL INSTALLATION

LIGHTING AND POWER LAYOUT

3RD STOREY PLAN DECK 5 & DECK 6

SCALE:

AS SHOWN

DATE:

NOVEMBER 2025

DRAWN BY:

TLY

CHECKED BY:

JL/NC

M & E CONSULTANT:

CCAPpartners

CCA & Partners Pte Ltd
M&E Consulting Engineer
46 Lorong 17 Geylang, #02-02, Enterprise Industrial Building,
Singapore 388568, Tel: 6476 2272 Fax: 6475 6229
E-mail : cca@cheetoon.com

C&S ENGINEER:

ANG & ONG
CONSULTANTS PTE LTD

(Professional Engineers, Project Management and
and Structural Inspection)

Blk 28, Sin Ming Lane,
#07-137, Midview City,
Singapore 573972
Tel: (65) 6459 5438 Fax: (65) 6459 5267
Email: info@aoconsultants.com

QUANTITY SURVEYOR:

QS Consultants Pte Ltd

21 Bukit Batok Crescent
#16-70, WCEGA Tower
Singapore 658065
Tel: 6899 4298 Fax: 6899 4981
E-mail : qs@qsconsultants.sg

DRAWING NO. HB-N2303-B78-E-203 REVISION: -

DESIGN ENGINEER


QUALIFIED PERSON

	LED BULKHEAD LIGHT FITTING C/W BATTERY PACK (SURFACE MOUNTED)
---	--

The battery pack emergency LED light fittings are to be circuit to DB-CP3/L1 & DB-CP3/L2. Tenderers shall deem this requirement included in their scope of works, including all necessary cabling, terminations, and associated accessories for a complete and functional installation.



DESIGN ENGINEER	QUALIFIED PERSON
-----------------	------------------

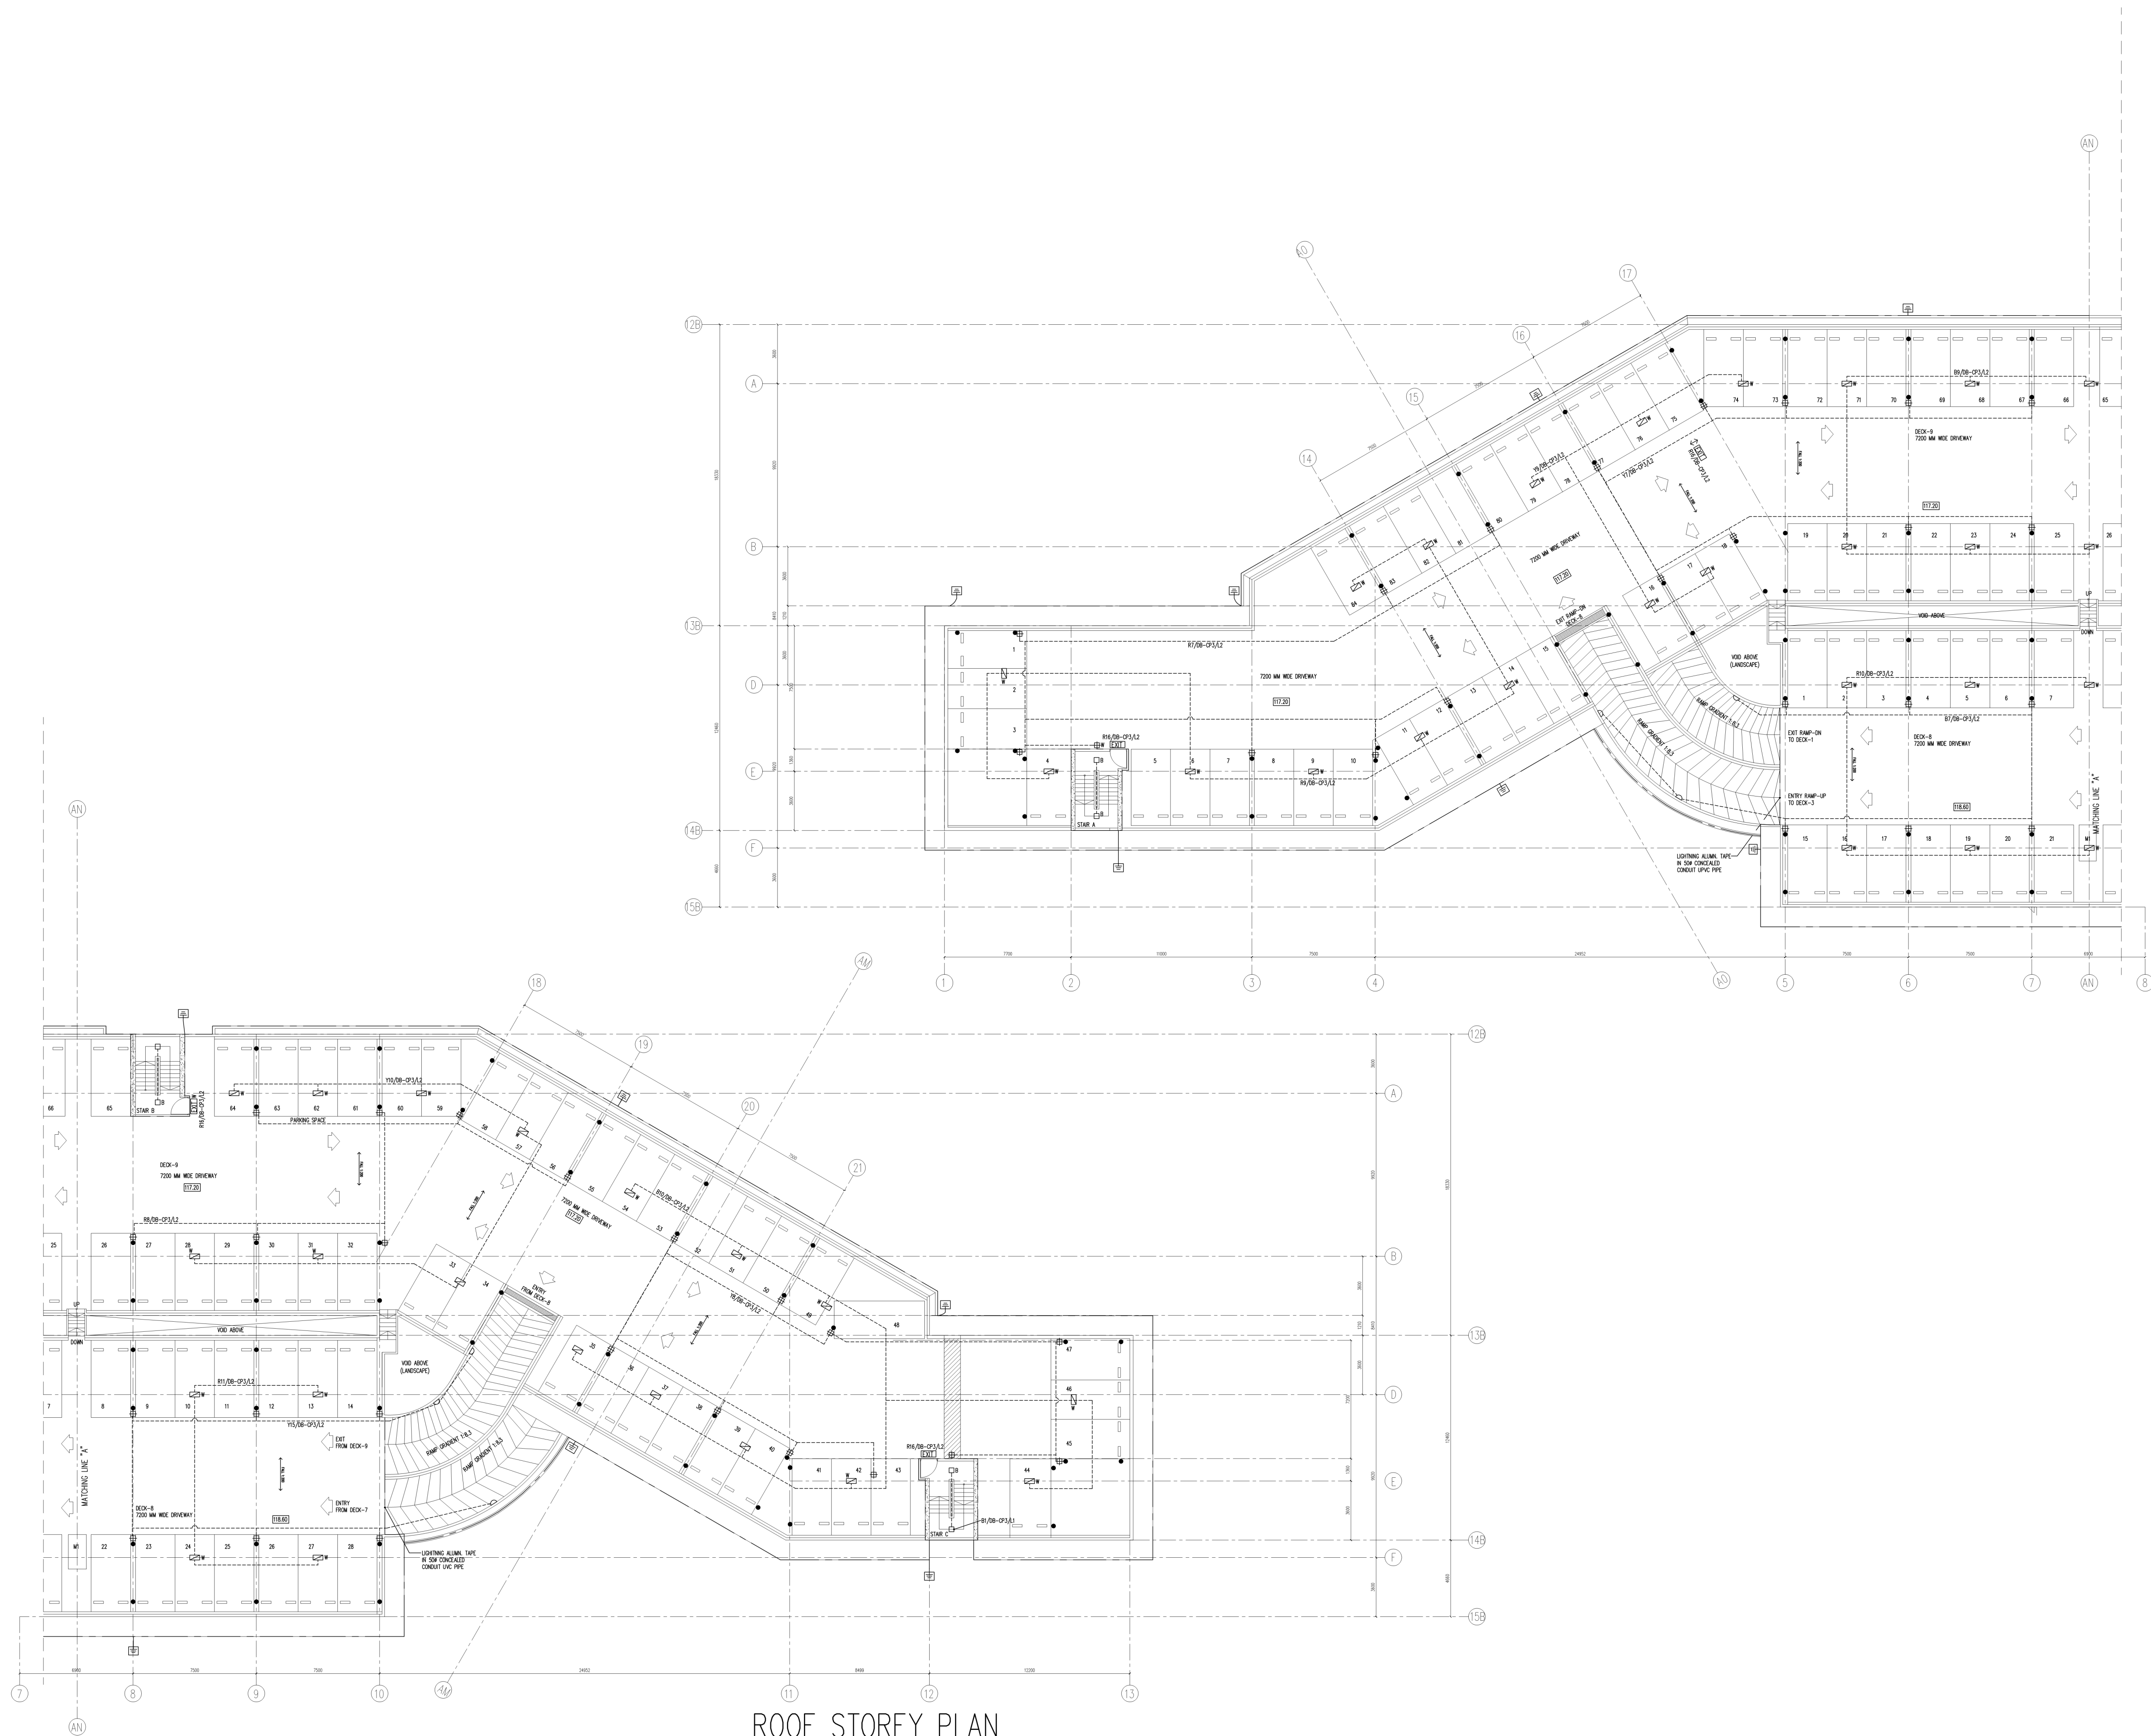

ROOF STOREY PLAN
DECK 8 & DECK 9
SCALE 1 : 200

TENDER DRAWING
NOVEMBER 2025

REV	DATE	DRAWN	CHECKED	DESCRIPTION
-----	------	-------	---------	-------------

TENDER DRAWING

CLIENT:



HDB HUB 480 LORONG 6 TOA PAYOH SINGAPORE 310480

CLIENT SIGNATURE:

DRAWING NO. HB-N2303-B78-E-205 REVISION: -

PROJECT TITLE:

MECHANICAL AND ELECTRICAL
CYCLICAL IMPROVEMENT WORKS
TO MULTI-STOREY CAR PARKS
(BATCH 34)

DRAWING TITLE: (FOR EST BLK NO 769AMSCP)
ELECTRICAL INSTALLATION
LIGHTING, POWER AND LIGHTNING PROTECTION LAYOUT
ROOF STOREY PLAN DECK 8 & DECK 9

SCALE: AS SHOWN DATE: NOVEMBER 2025

DRAWN BY: TLY CHECKED BY: JL/NC

M & E CONSULTANT:



CCA & Partners Pte Ltd
M&E Consulting Engineer
46 Lorong 17 Geylang, #02-02, Enterprise Industrial Building,
Singapore 388566, Tel: 6476 2272 Fax: 6475 6229
E-mail : cca@cheetoon.com

C&S ENGINEER:



(Professional Engineers, Project Management and
and Structural Inspection)

Blk 28, Sin Ming Lane,
#07-137, Midview City,
Singapore 573972
Tel: (65) 6459 5438 Fax: (65) 6459 5267
Email: info@aoconsultants.com

QUANTITY SURVEYOR:

QS Consultants Pte Ltd


21 Bukit Batok Crescent
#16-70, WCEGA Tower
Singapore 658065
Tel: 6899 4298 Fax: 6899 4981
E-mail : qs@qsconsultants.sg

DRAWING NO. HB-N2303-B78-E-205 REVISION: -

DESIGN ENGINEER QUALIFIED PERSON

LEGEND

	HRC FUSE (RATING AS SHOWN)		AMMETER		INVERSE DEFINITE MINIMUM TIME-LAG EARTH FAULT RELAY OF 3/10 CHARACTERISTIC C/W INSTANTANEOUS HIGH SET ELEMENT
	MOULDED CASE CIRCUIT BREAKER/ MINIATURE CIRCUIT BREAKER		VOLTMETER		OVERCURRENT RELAY
	RESIDUAL CURRENT CIRCUIT BREAKER		VOLTMETER SELECTOR SWITCH (L1L2-L2L3-L3L1, L1N, L2N, L3N, OFF)		EARTH FAULT RELAY
	ISOLATOR		AMMETER SELECTOR SWITCH (L1-L2-L3-OFF)		INDICATING LIGHT (LED)
	CONTACTOR		CURRENT TRANSFORMER		EARTHING
	KILOWATT-HOUR METER		ZERO PHASE SEQUENCE CURRENT TRANSFORMER		TIME SWITCH
	DIGITAL POWER METER		EARTH LEAKAGE RELAY C/W TIME LAG (10A TYPE)		BY-PASS SWITCH
	AMMETER C/W MAXIMUM DEMAND INDICATOR		INVERSE DEFINITE MINIMUM TIME-LAG OVERCURRENT RELAY OF 3/10 CHARACTERISTIC C/W INSTANTANEOUS HIGH SET ELEMENT		

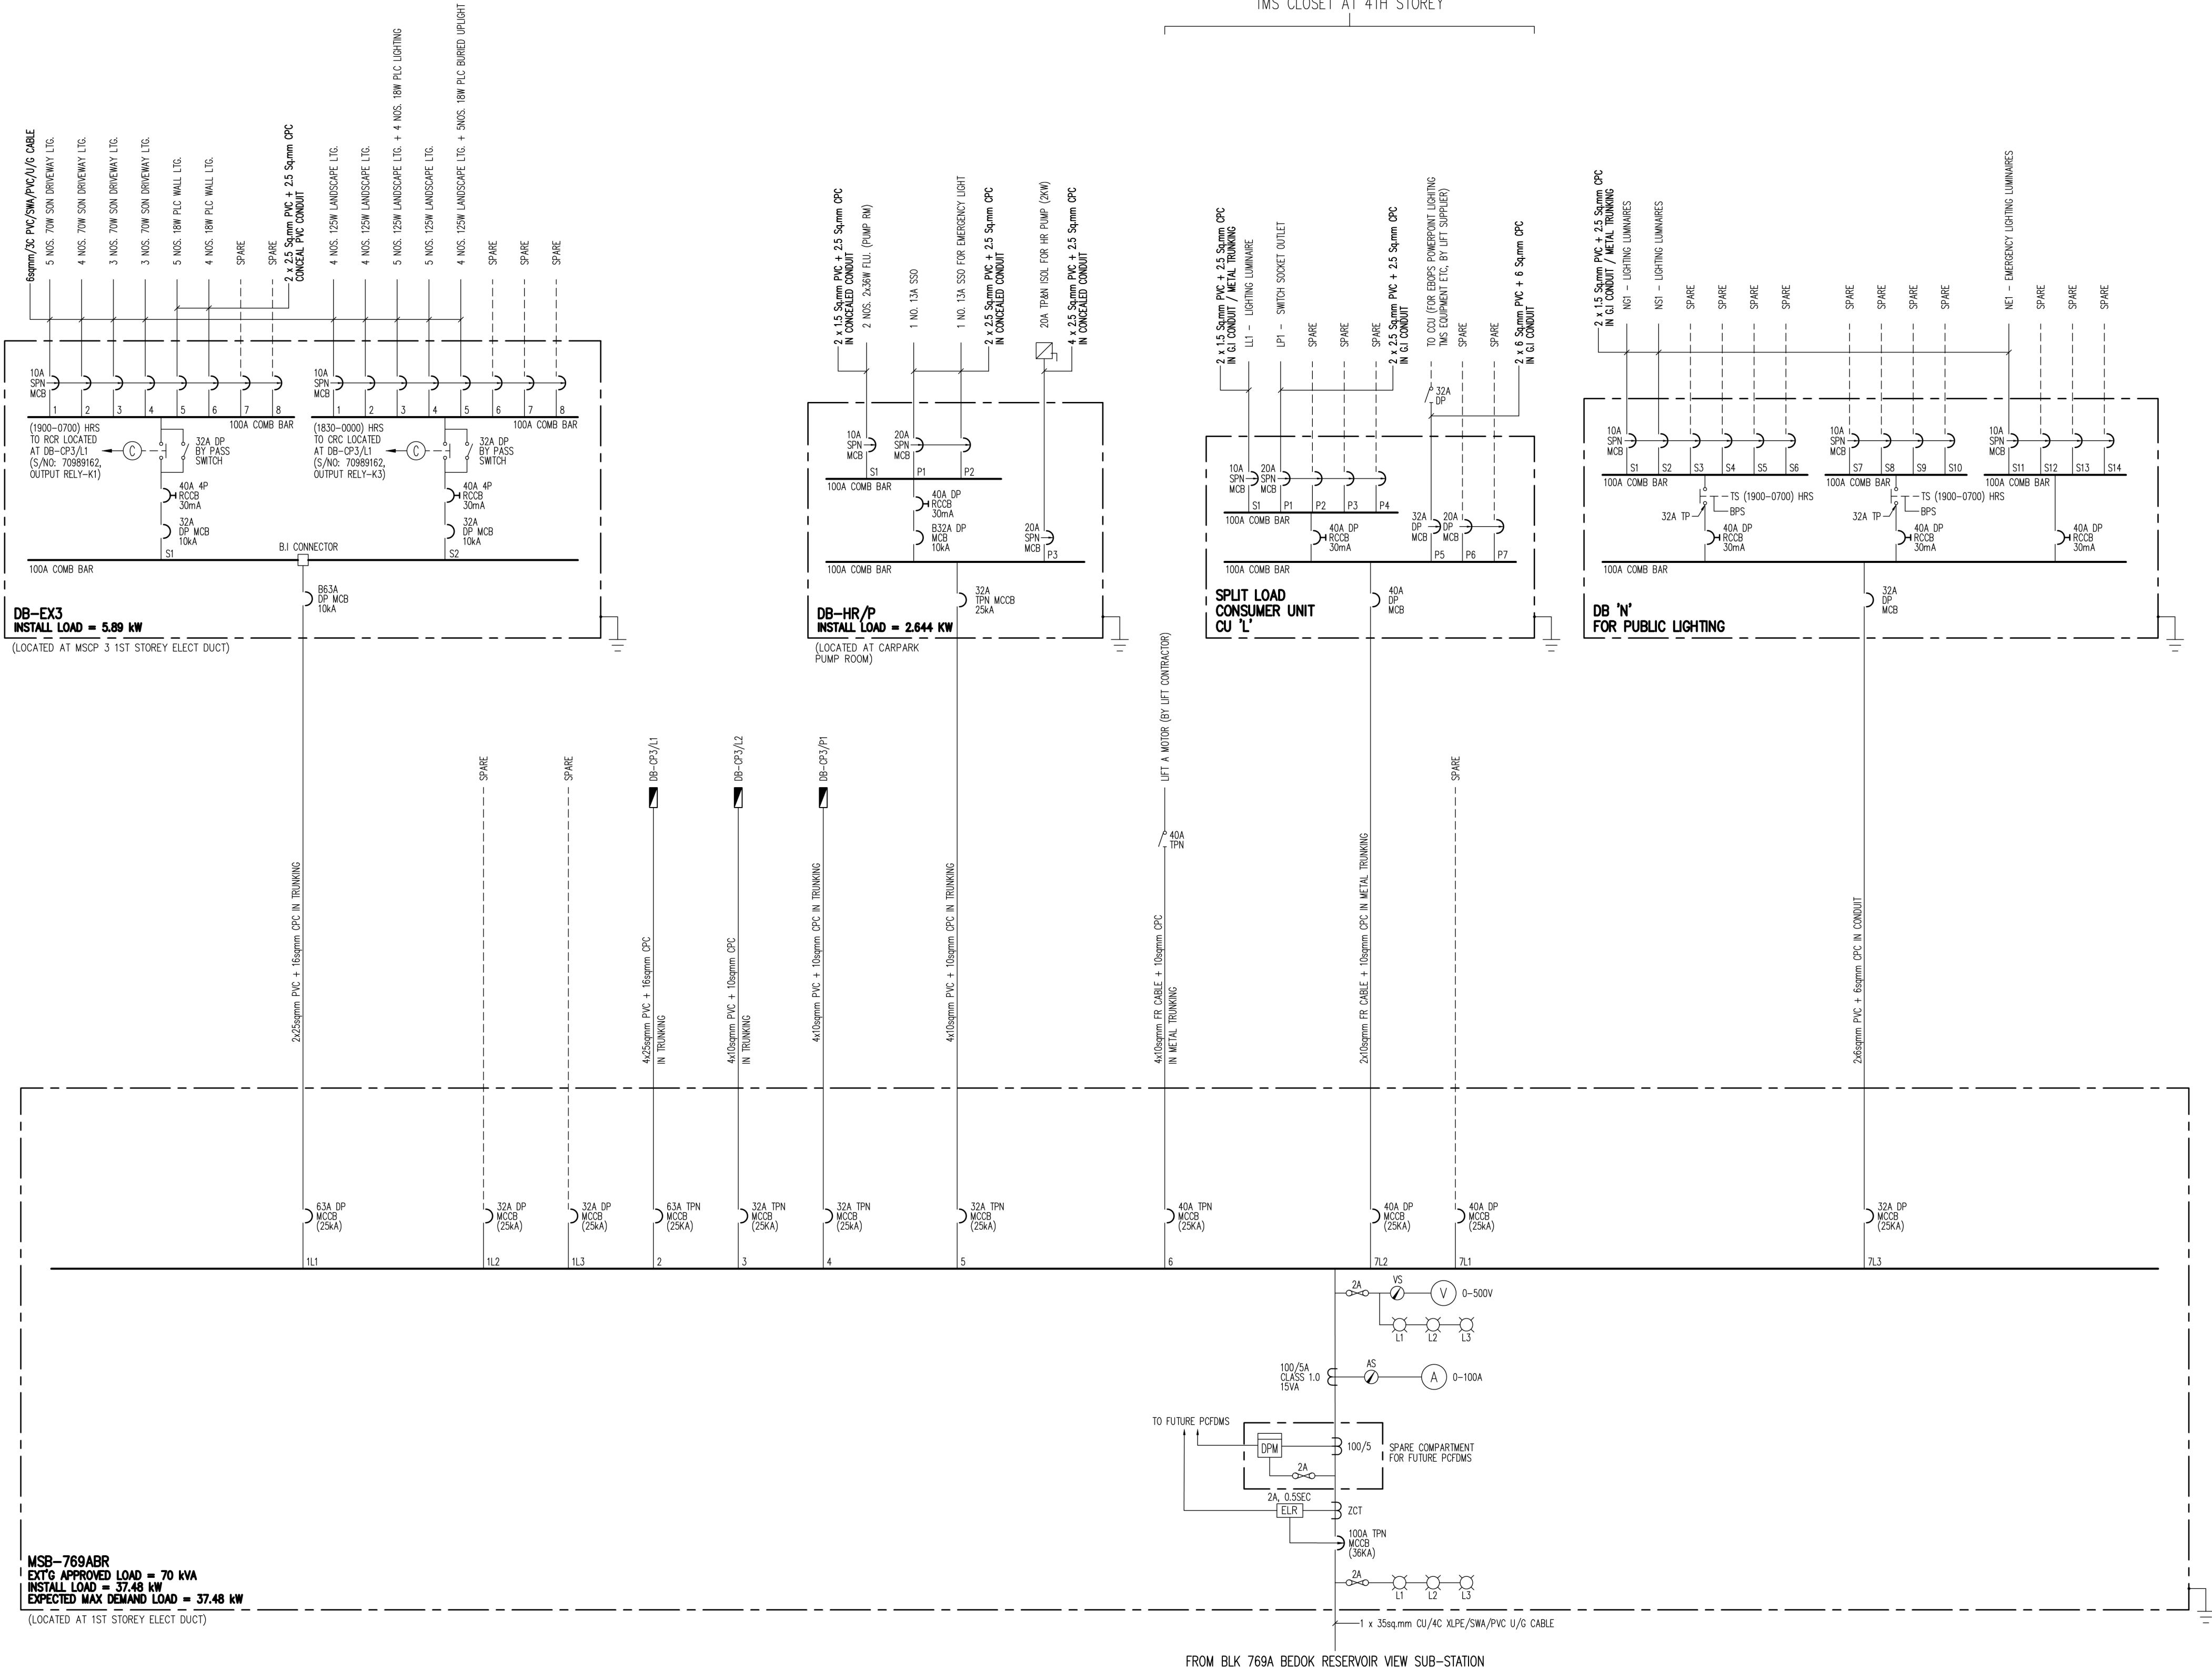

TENDER DRAWING
NOVEMBER 2025

REV	DATE	DRAWN	CHECKED	DESCRIPTION
-----	------	-------	---------	-------------

TENDER DRAWING

CLIENT:



HDB HUB 480 LORONG 6 TOA PAYOH SINGAPORE 310480

CLIENT SIGNATURE:

DRAWING NO. HB-N2303-B78-E-301 REVISION: -

PROJECT TITLE:

MECHANICAL AND ELECTRICAL
CYCLICAL IMPROVEMENT WORKS
TO MULTI-STOREY CAR PARKS
(BATCH 34)

DRAWING TITLE: (FOR EST BLK NO 769AMSCP)

ELECTRICAL INSTALLATION

LV SINGLE LINE DIAGRAM 1

SCALE: N T S DATE: NOVEMBER 2025

DRAWN BY: TLY CHECKED BY: JL/NC

M & E CONSULTANT:



CCA & Partners Pte Ltd
M&E Consulting Engineer
46 Lorong 17 Geylang, #02-02, Enterprise Industrial Building,
Singapore 388568, Tel: 6476 2272 Fax: 6475 6229
E-mail : cca@cheetoon.com

C&S ENGINEER:



(Professional Engineers, Project Management and
and Structural Inspection)

Blk 28, Sin Ming Lane,
#07-137, Midview City,
Singapore 573972
Tel: (65) 6459 5438 Fax: (65) 6459 5267
Email: info@aoconsultants.com

QUANTITY SURVEYOR:

QS Consultants Pte Ltd


21 Bukit Batok Crescent
#16-70, WCEGA Tower
Singapore 658065
Tel: 6899 4298 Fax: 6899 4981
E-mail : qs@qsconsultants.sg

DRAWING NO. HB-N2303-B78-E-301 REVISION: -

DESIGN ENGINEER QUALIFIED PERSON

© copyright cca & partners pte ltd

	HRC FUSE (RATING AS SHOWN)		AMMETER		INVERSE DEFINITE MINIMUM TIME-LAG EARTH FAULT RELAY OF 3/10 CHARACTERISTIC C/W INSTANTANEOUS HIGH SET ELEMENT
	MOULDED CASE CIRCUIT BREAKER/ MINIATURE CIRCUIT BREAKER		VOLTMETER		OVERCURRENT RELAY
	RESIDUAL CURRENT CIRCUIT BREAKER		VOLTMETER SELECTOR SWITCH (L1L2-L2L3-L3L1, L1N, L2N, L3N, OFF)		EARTH FAULT RELAY
	ISOLATOR		AMMETER SELECTOR SWITCH (L1-L2-L3-OFF)		INDICATING LIGHT (LED)
	CONTACTOR		CURRENT TRANSFORMER		EARTHING
	KILOWATT-HOUR METER		ZERO PHASE SEQUENCE CURRENT TRANSFORMER	TS	TIME SWITCH
	DIGITAL POWER METER		EARTH LEAKAGE RELAY C/W TIME LAG (10A TYPE)	BPS	BY-PASS SWITCH
	AMMETER C/W MAXIMUM DEMAND INDICATOR		INVERSE DEFINITE MINIMUM TIME-LAG OVERCURRENT RELAY OF 3/10 CHARACTERISTIC C/W INSTANTANEOUS HIGH SET ELEMENT		

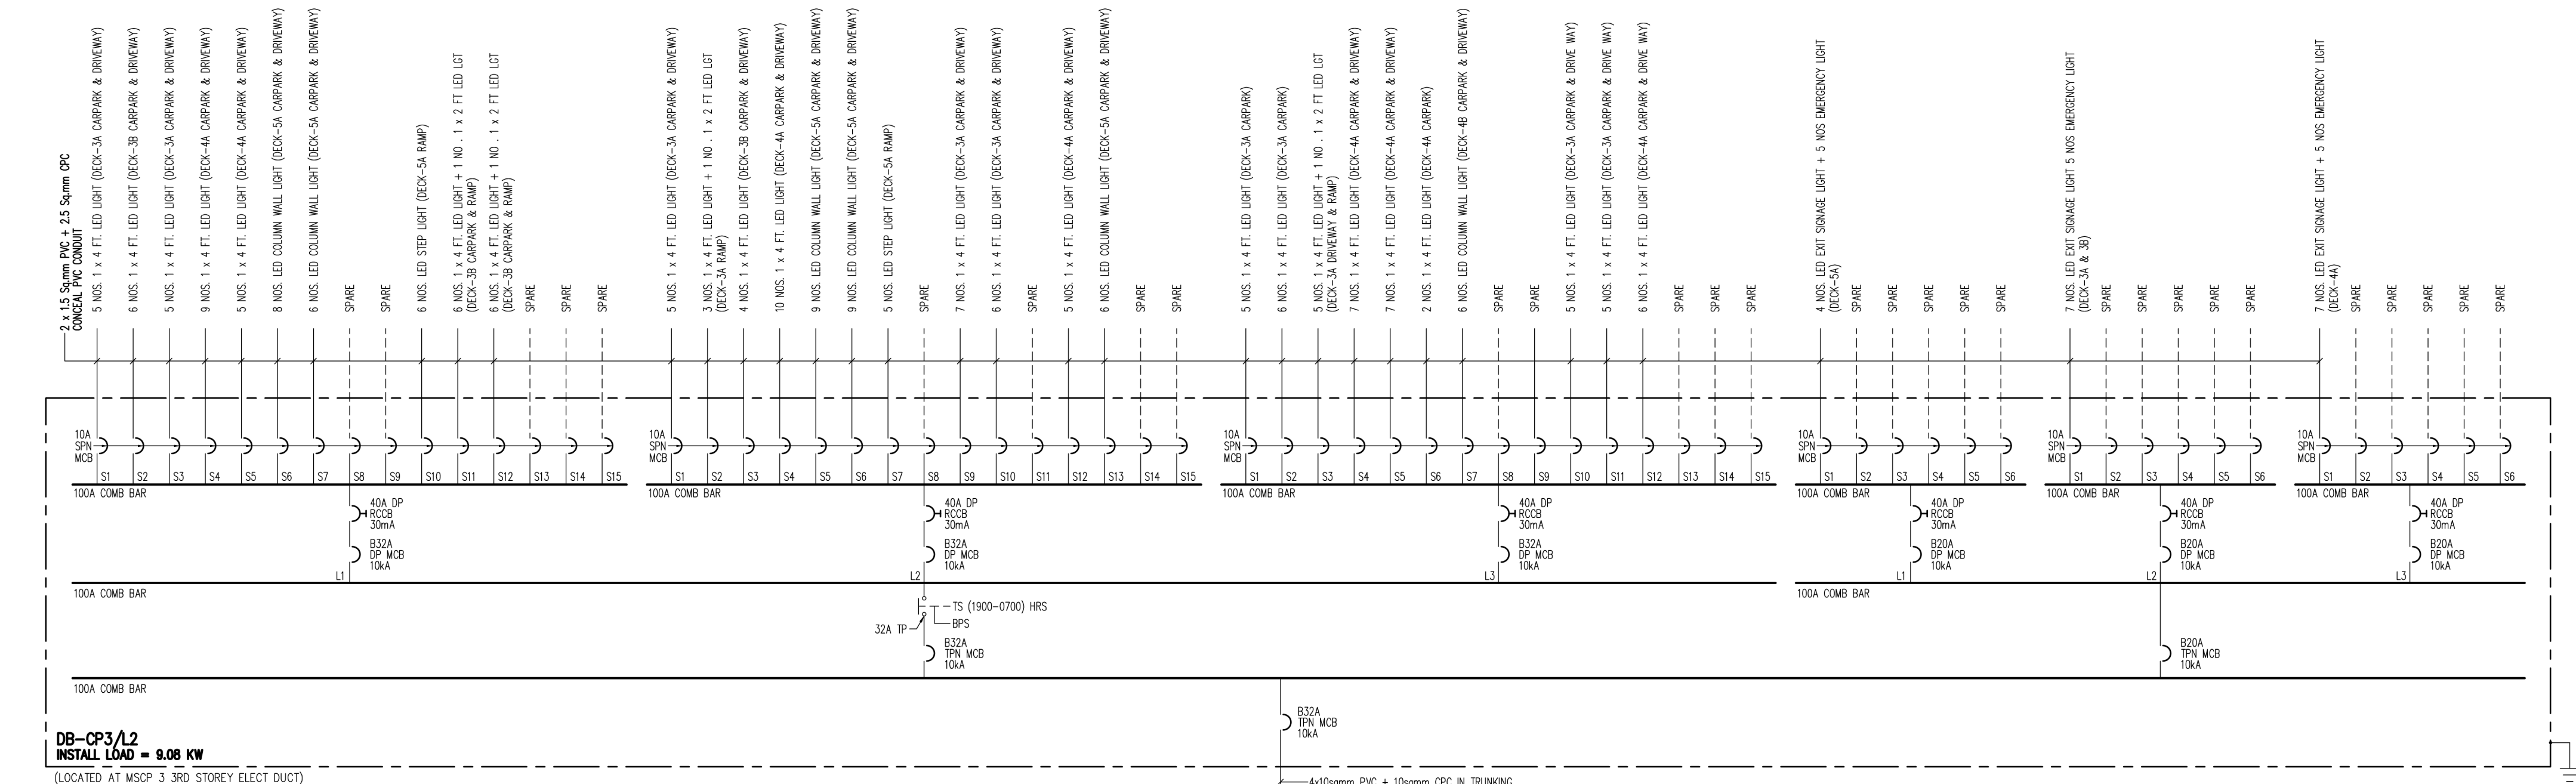

REV	DATE	DRAWN	CHECKED	DESCRIPTION
-----	------	-------	---------	-------------

TENDER DRAWING

CLIENT:



HDB HUB 480 LORONG 6 TOA PAYOH SINGAPORE 310480

CLIENT SIGNATURE:

DRAWING NO. HB-N2303-B78-E-302	REVISION: -
--------------------------------	-------------

PROJECT TITLE:

MECHANICAL AND ELECTRICAL
CYCLICAL IMPROVEMENT WORKS
TO MULTI-STOREY CAR PARKS
(BATCH 34)

DRAWING TITLE: (FOR EST BLK NO 769AMSCP)

ELECTRICAL INSTALLATION

LV SINGLE LINE DIAGRAM 2

SCALE: N T S	DATE: NOVEMBER 2025
DRAWN BY: TLY	CHECKED BY: JL/NC

M & E CONSULTANT:

CCAPartners

CCA & Partners Pte Ltd
M&E Consulting Engineer
46 Lorong 17 Geylang, #02-02, Enterprise Industrial Building,
Singapore 388568, Tel: 6476 2272 Fax: 6475 6229
E-mail : cca@cheechoon.com

C&S ENGINEER:



(Professional Engineers, Project Management and
and Structural Inspection)

Blk 28, Sin Ming Lane,
#07-137, Midview City,
Singapore 573972
Tel: (65) 6459 5438 Fax: (65) 6459 5267
Email: info@aaoconsults.com

QUANTITY SURVEYOR:


QS Consultants Pte Ltd

21 Bukit Batok Crescent
#16-70, WCEGA Tower
Singapore 658065
Tel: 6899 4298 Fax: 6899 4981
E-mail : qs@qsconsultants.sg

DRAWING NO. HB-N2303-B78-E-302	REVISION: -
--------------------------------	-------------

DESIGN ENGINEER

QUALIFIED PERSON

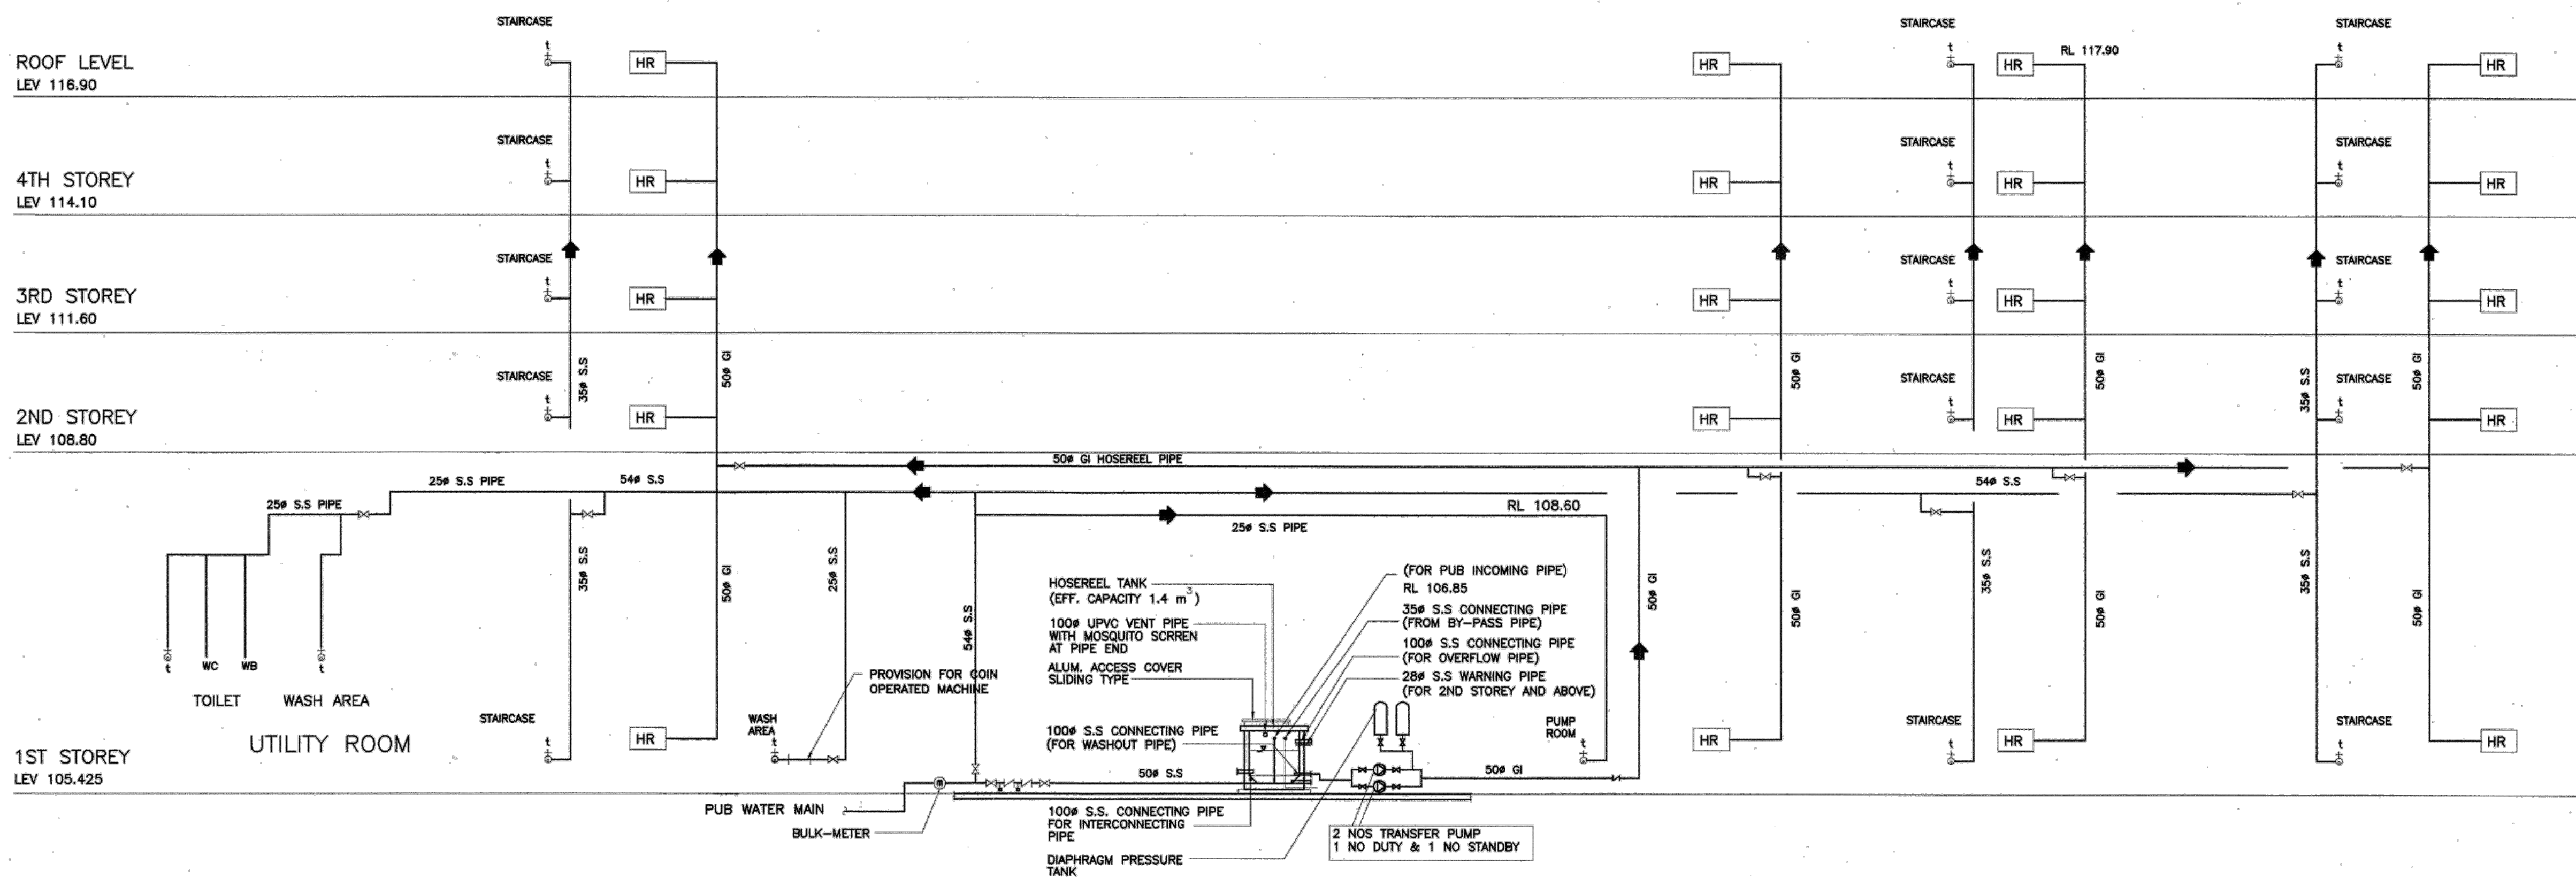

TYPICAL MULTISTOREY CARPARK
(MSCP 769A)

TENDER DRAWING
NOVEMBER 2025

REV DATE DRAWN CHECKED DESCRIPTION

TENDER DRAWING

CLIENT:



HDB HUB 480 LORONG 6 TOA PAYOH SINGAPORE 310480

CLIENT SIGNATURE:

DRAWING NO. HB-N2303-B78-FP-301 REVISION: -

PROJECT TITLE:

MECHANICAL AND ELECTRICAL
CYCLICAL IMPROVEMENT WORKS
TO MULTI-STOREY CAR PARKS
(BATCH 34)

DRAWING TITLE: (FOR EST BLK NO 769AMSCP)

FIRE PROTECTION INSTALLATION

FIRE ALARM LAYOUT

HOSEREEL SCHEMATIC DIAGRAM

SCALE: AS SHOWN DATE: NOVEMBER 2025

DRAWN BY: SL CHECKED BY: JL/NC

M & E CONSULTANT:



CCA & Partners Pte Ltd
M&E Consulting Engineer
46 Lorong 17 Geylang, #02-02, Enterprise Industrial Building,
Singapore 388566, Tel: 6476 2272 Fax: 6475 6229
E-mail: cca@chechoon.com

C&S ENGINEER:



(Professional Engineers, Project Management and
and Structural Inspection)

Blk 28, Sin Ming Lane,
#07-137, Midview City,
Singapore 573972
Tel: (65) 6459 5438 Fax: (65) 6459 5267
Email: info@aoconsultants.com

QUANTITY SURVEYOR:

QS Consultants Pte Ltd

21 Bukit Batok Crescent
#16-70, WCEGA Tower
Singapore 658065
Tel: 6899 4298 Fax: 6899 4981
E-mail: qs@qsconsultants.sg



DRAWING NO. HB-N2303-B78-FP-301 REVISION: -

DESIGN ENGINEER QUALIFIED PERSON


LEGEND	
	LED BULKHEAD LIGHT FITTING C/W BATTERY PACK (SURFACE MOUNTED)

Note:

The battery pack emergency LED light fittings are to be circuit to DB-CP3/L1 & DB-CP3/L2. Tenderers shall deem this requirement included in their scope of works, including all necessary cabling, terminations, and associated accessories for a complete and functional installation.

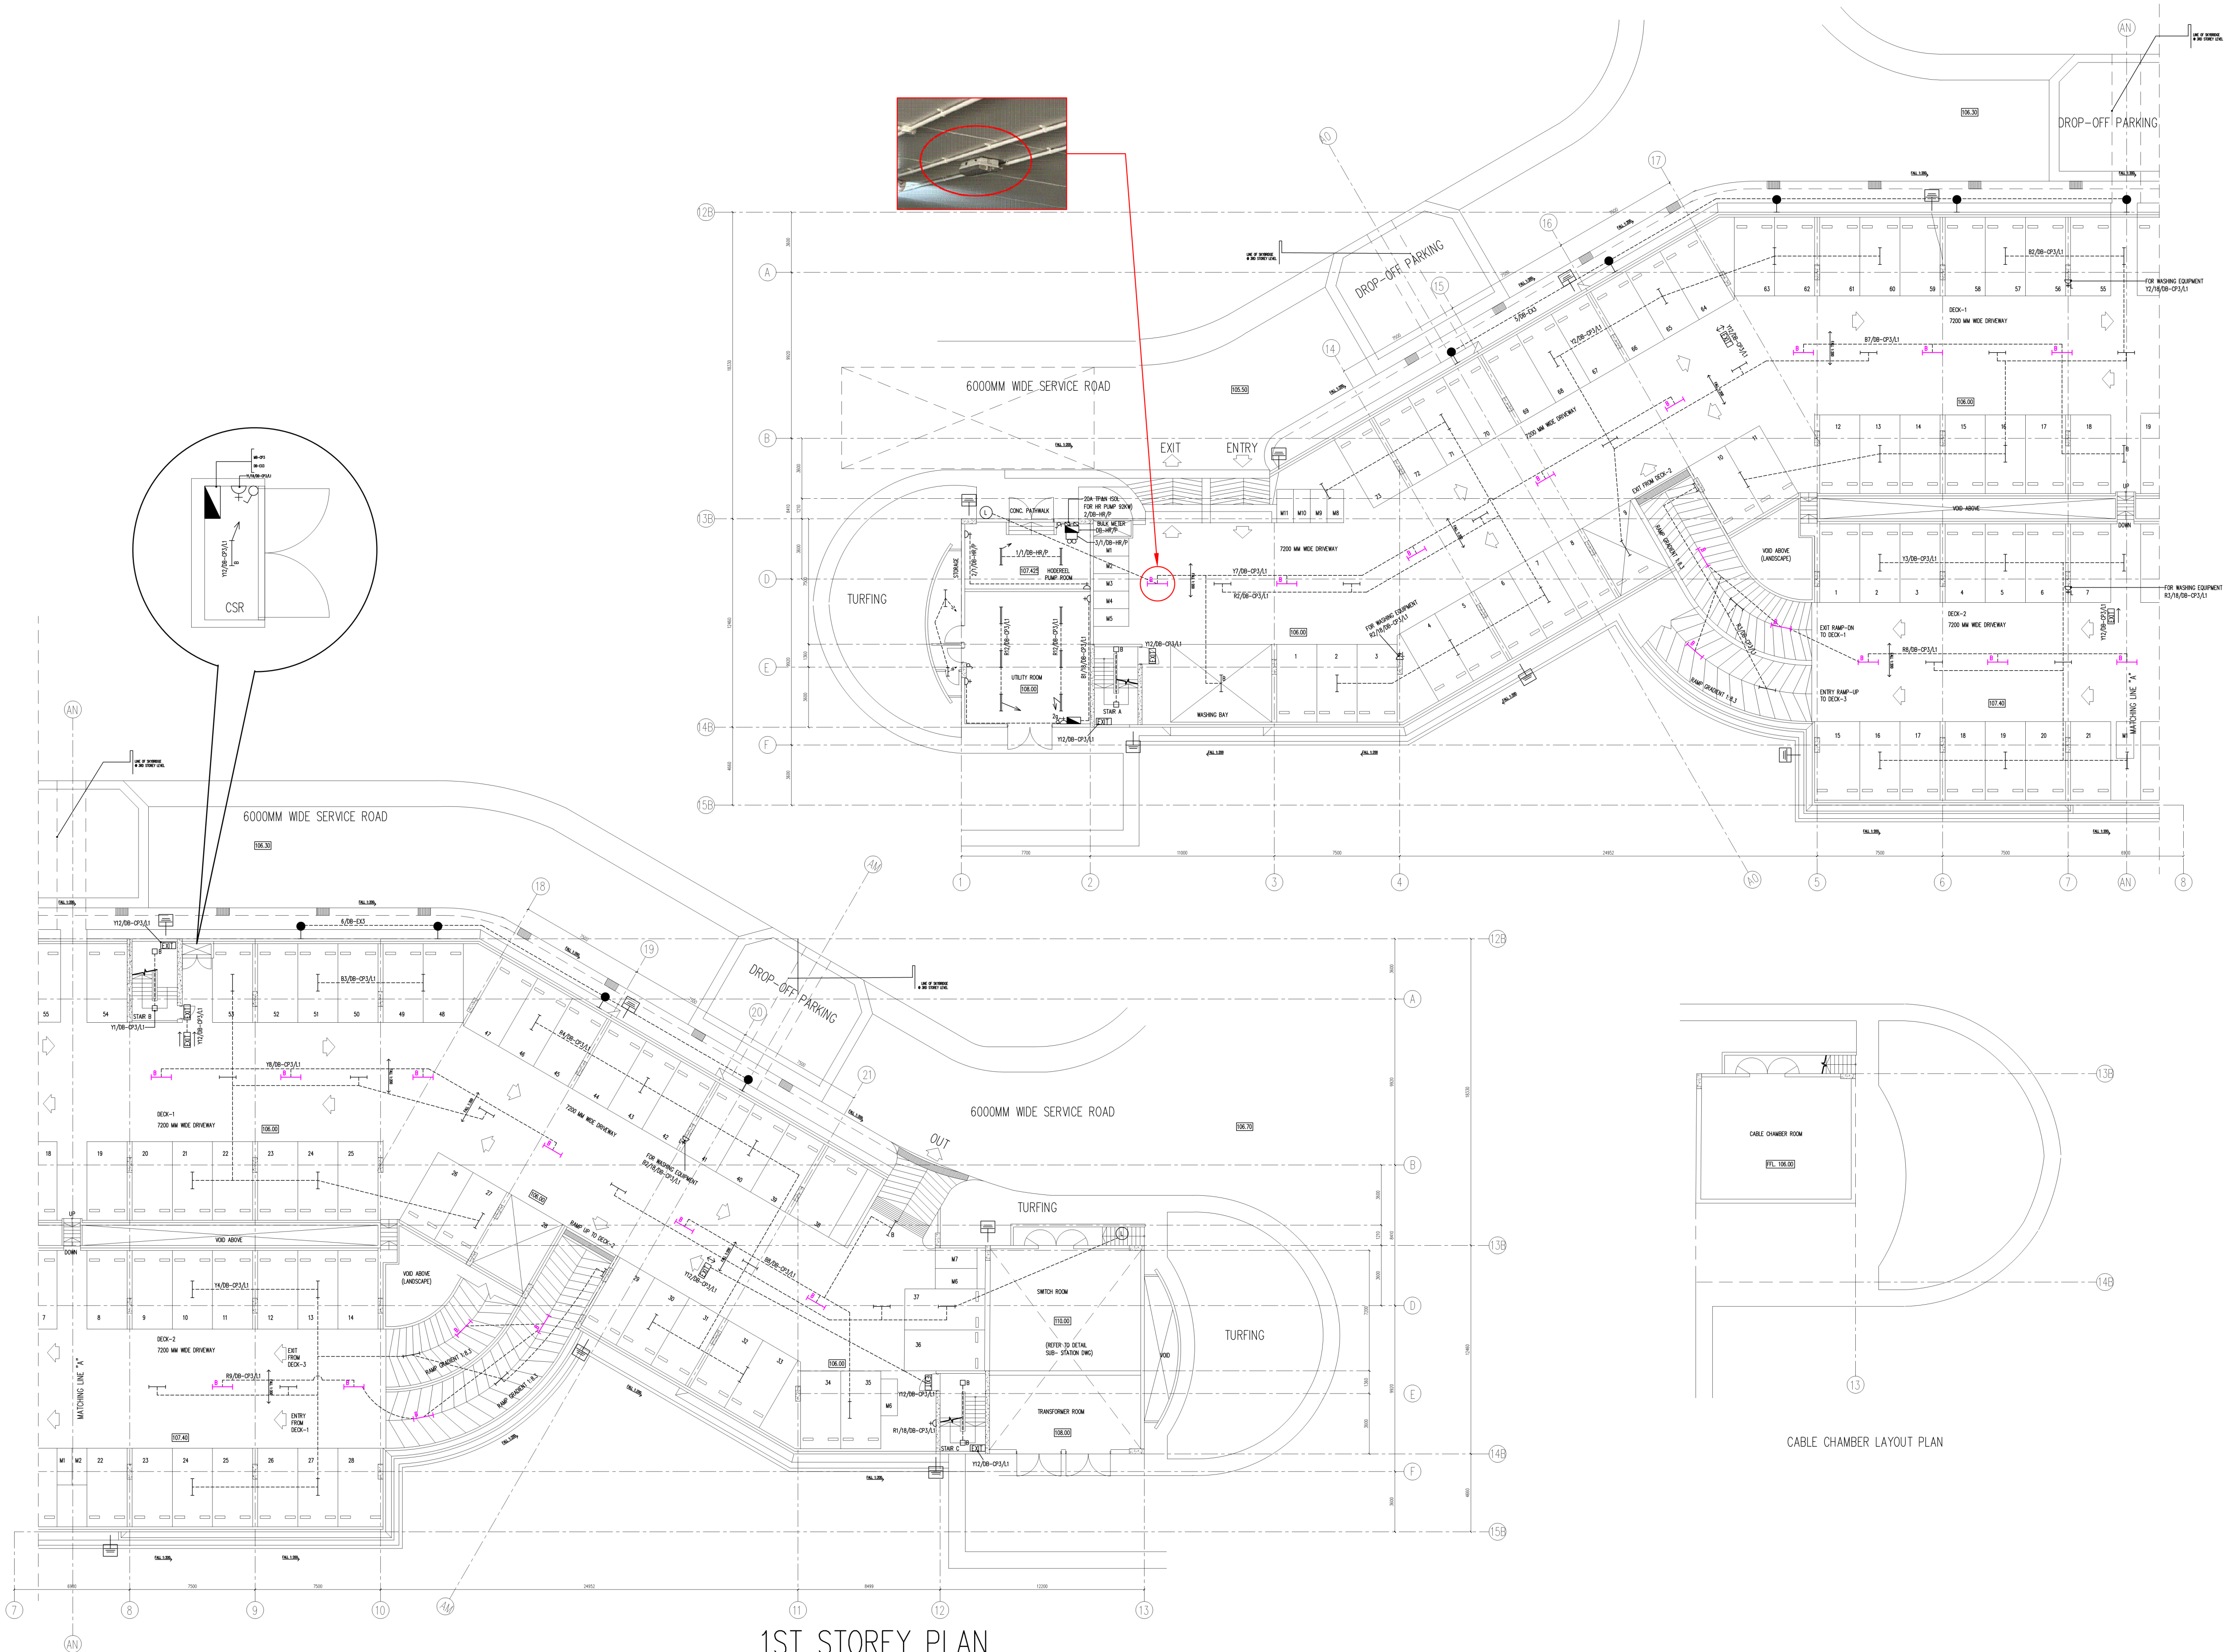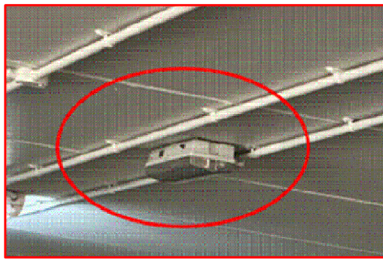

1ST STOREY PLAN
DECK 1 & DECK 2
SCALE 1 : 200

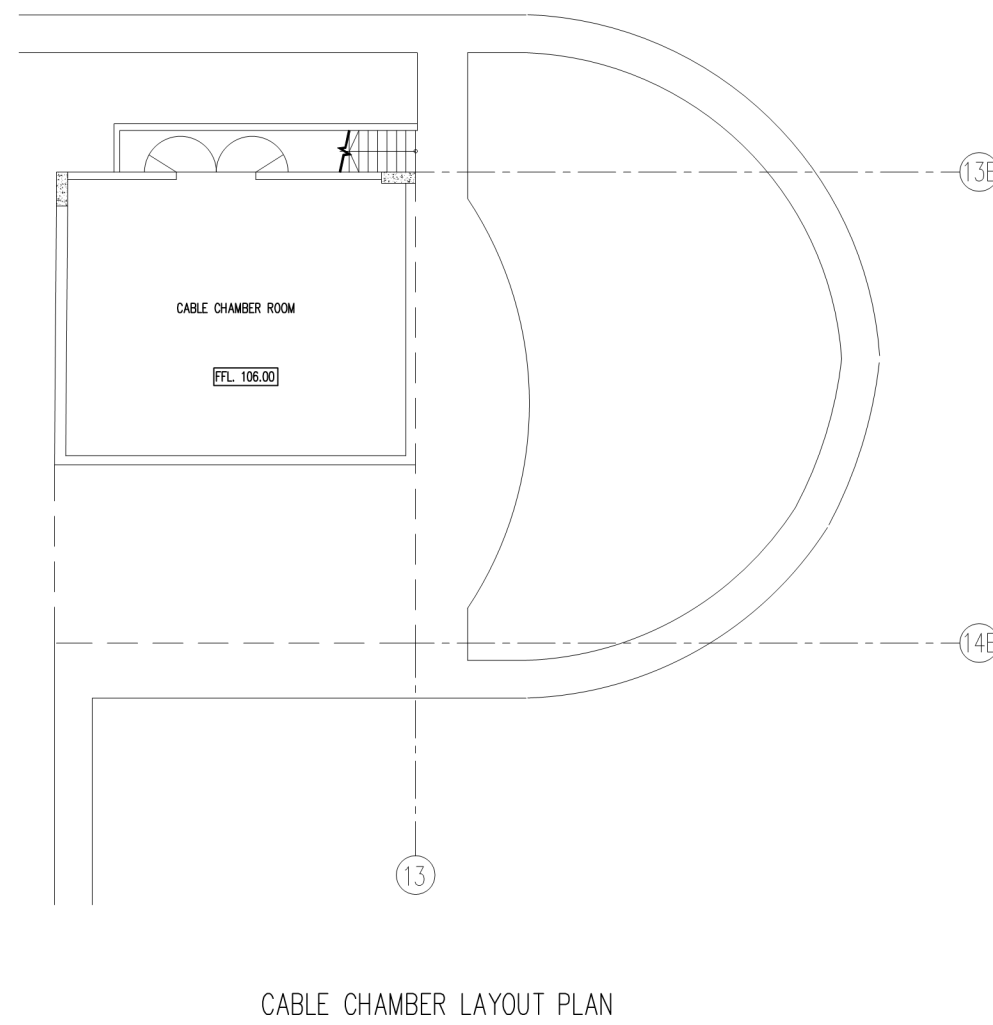

TENDER DRAWING
NOVEMBER 2025

REV DATE DRAWN CHECKED DESCRIPTION

TENDER DRAWING

CLIENT:



HDB HUB 480 LORONG 6 TOA PAYOH SINGAPORE 310480

CLIENT SIGNATURE:

DRAWING NO. HB-N2303-B78-E-201

REVISION: -

PROJECT TITLE:

MECHANICAL AND ELECTRICAL
CYCLICAL IMPROVEMENT WORKS
TO MULTI-STORY CAR PARKS
(BATCH 34)

DRAWING TITLE: (FOR EST BLK NO 769AMSCP)

ELECTRICAL INSTALLATION
LIGHTING, POWER AND LIGHTNING PROTECTION LAYOUT
1ST STOREY PLAN DECK 1 & DECK 2

SCALE:

AS SHOWN

DATE:

NOVEMBER 2025

DRAWN BY:

TLY

CHECKED BY:

JL/NC

M & E CONSULTANT:



CCA & Partners Pte Ltd
M&E Consulting Engineer
46 Lorong 17 Geylang, #02-02, Enterprise Industrial Building,
Singapore 388568, Tel: 6476 2272 Fax: 6475 6229
E-mail : cca@cheecheon.com

C&S ENGINEER:



(Professional Engineers, Project Management and
and Structural Inspection)

Blk 28, Sin Ming Lane,
#07-137, Midview City,
Singapore 573972
Tel: (65) 6459 5438 Fax: (65) 6459 5267
Email: info@aaoconsults.com

QUANTITY SURVEYOR:

QS Consultants Pte Ltd

21 Bukit Batok Crescent
#16-70, WCEGA Tower
Singapore 658065
Tel: 6899 4298 Fax: 6899 4981
E-mail : qs@qsconsultants.sg

DRAWING NO. HB-N2303-B78-E-201

REVISION: -

DESIGN ENGINEER

QUALIFIED PERSON